

2'661'000

Kanton Obwalden

Sanierung Älggistrasse

**SITUATION PLAN 1:2'000**  
(Plangrösse A3)

**Profil 51-54: Äggi Parkplatz bis Furt Älggibach 410 m**

Bauprojekt 21.11.2025

Bauherrschaft:

Korporation Sachseln  
Chalchhofen 1, 6073 Flüeli-Ranft  
Tel. 041 662 20 90  
E-Mail: [info@korporation-sachseln.ch](mailto:info@korporation-sachseln.ch)

Projektverfasser:

Adrian von Moos, dipl. Forsting. ETH  
Riedweg 3, 6072 Sachseln  
Tel. 079 726 98 16  
E-Mail: [adrian.vonmoos@bluewin.ch](mailto:adrian.vonmoos@bluewin.ch)

*Adrian von Moos*

*[Signature]*

## Massnahmen

- 1-54 Nummerierung  
(Detailbeschreibung siehe Massnahmenabelle)
- Auf Bergseite Böschung abflachen/Lichttraumprofil erstellen
  - Auf Talseite Böschung/Bankett verstärken
  - Steinblockmauern
  - Tragschicht Materialersatz
  - Durchlass bestehend teilweise mit Massnahme
  - Durchlass bestehend ersetzen / Durchlass neu
  - offene Gräben nachziehen/neu erstellen
  - Sickerleitung neu



1:2'000

0 10 20 30 40 50 Meter

Orthophoto 2018 © GIS-Daten AG


51-54:  
Bestehende Zementstabilisierung ersetzen durch  
Betonfahrspuren mit Mittelstreifen begrünt  
(Länge 410 m, Breite 80 + 100 + 80 cm = 260 cm)

Betonfahrbahn  
bei Abzweigung

Furt Älggibach

1'183'000

2'661'000

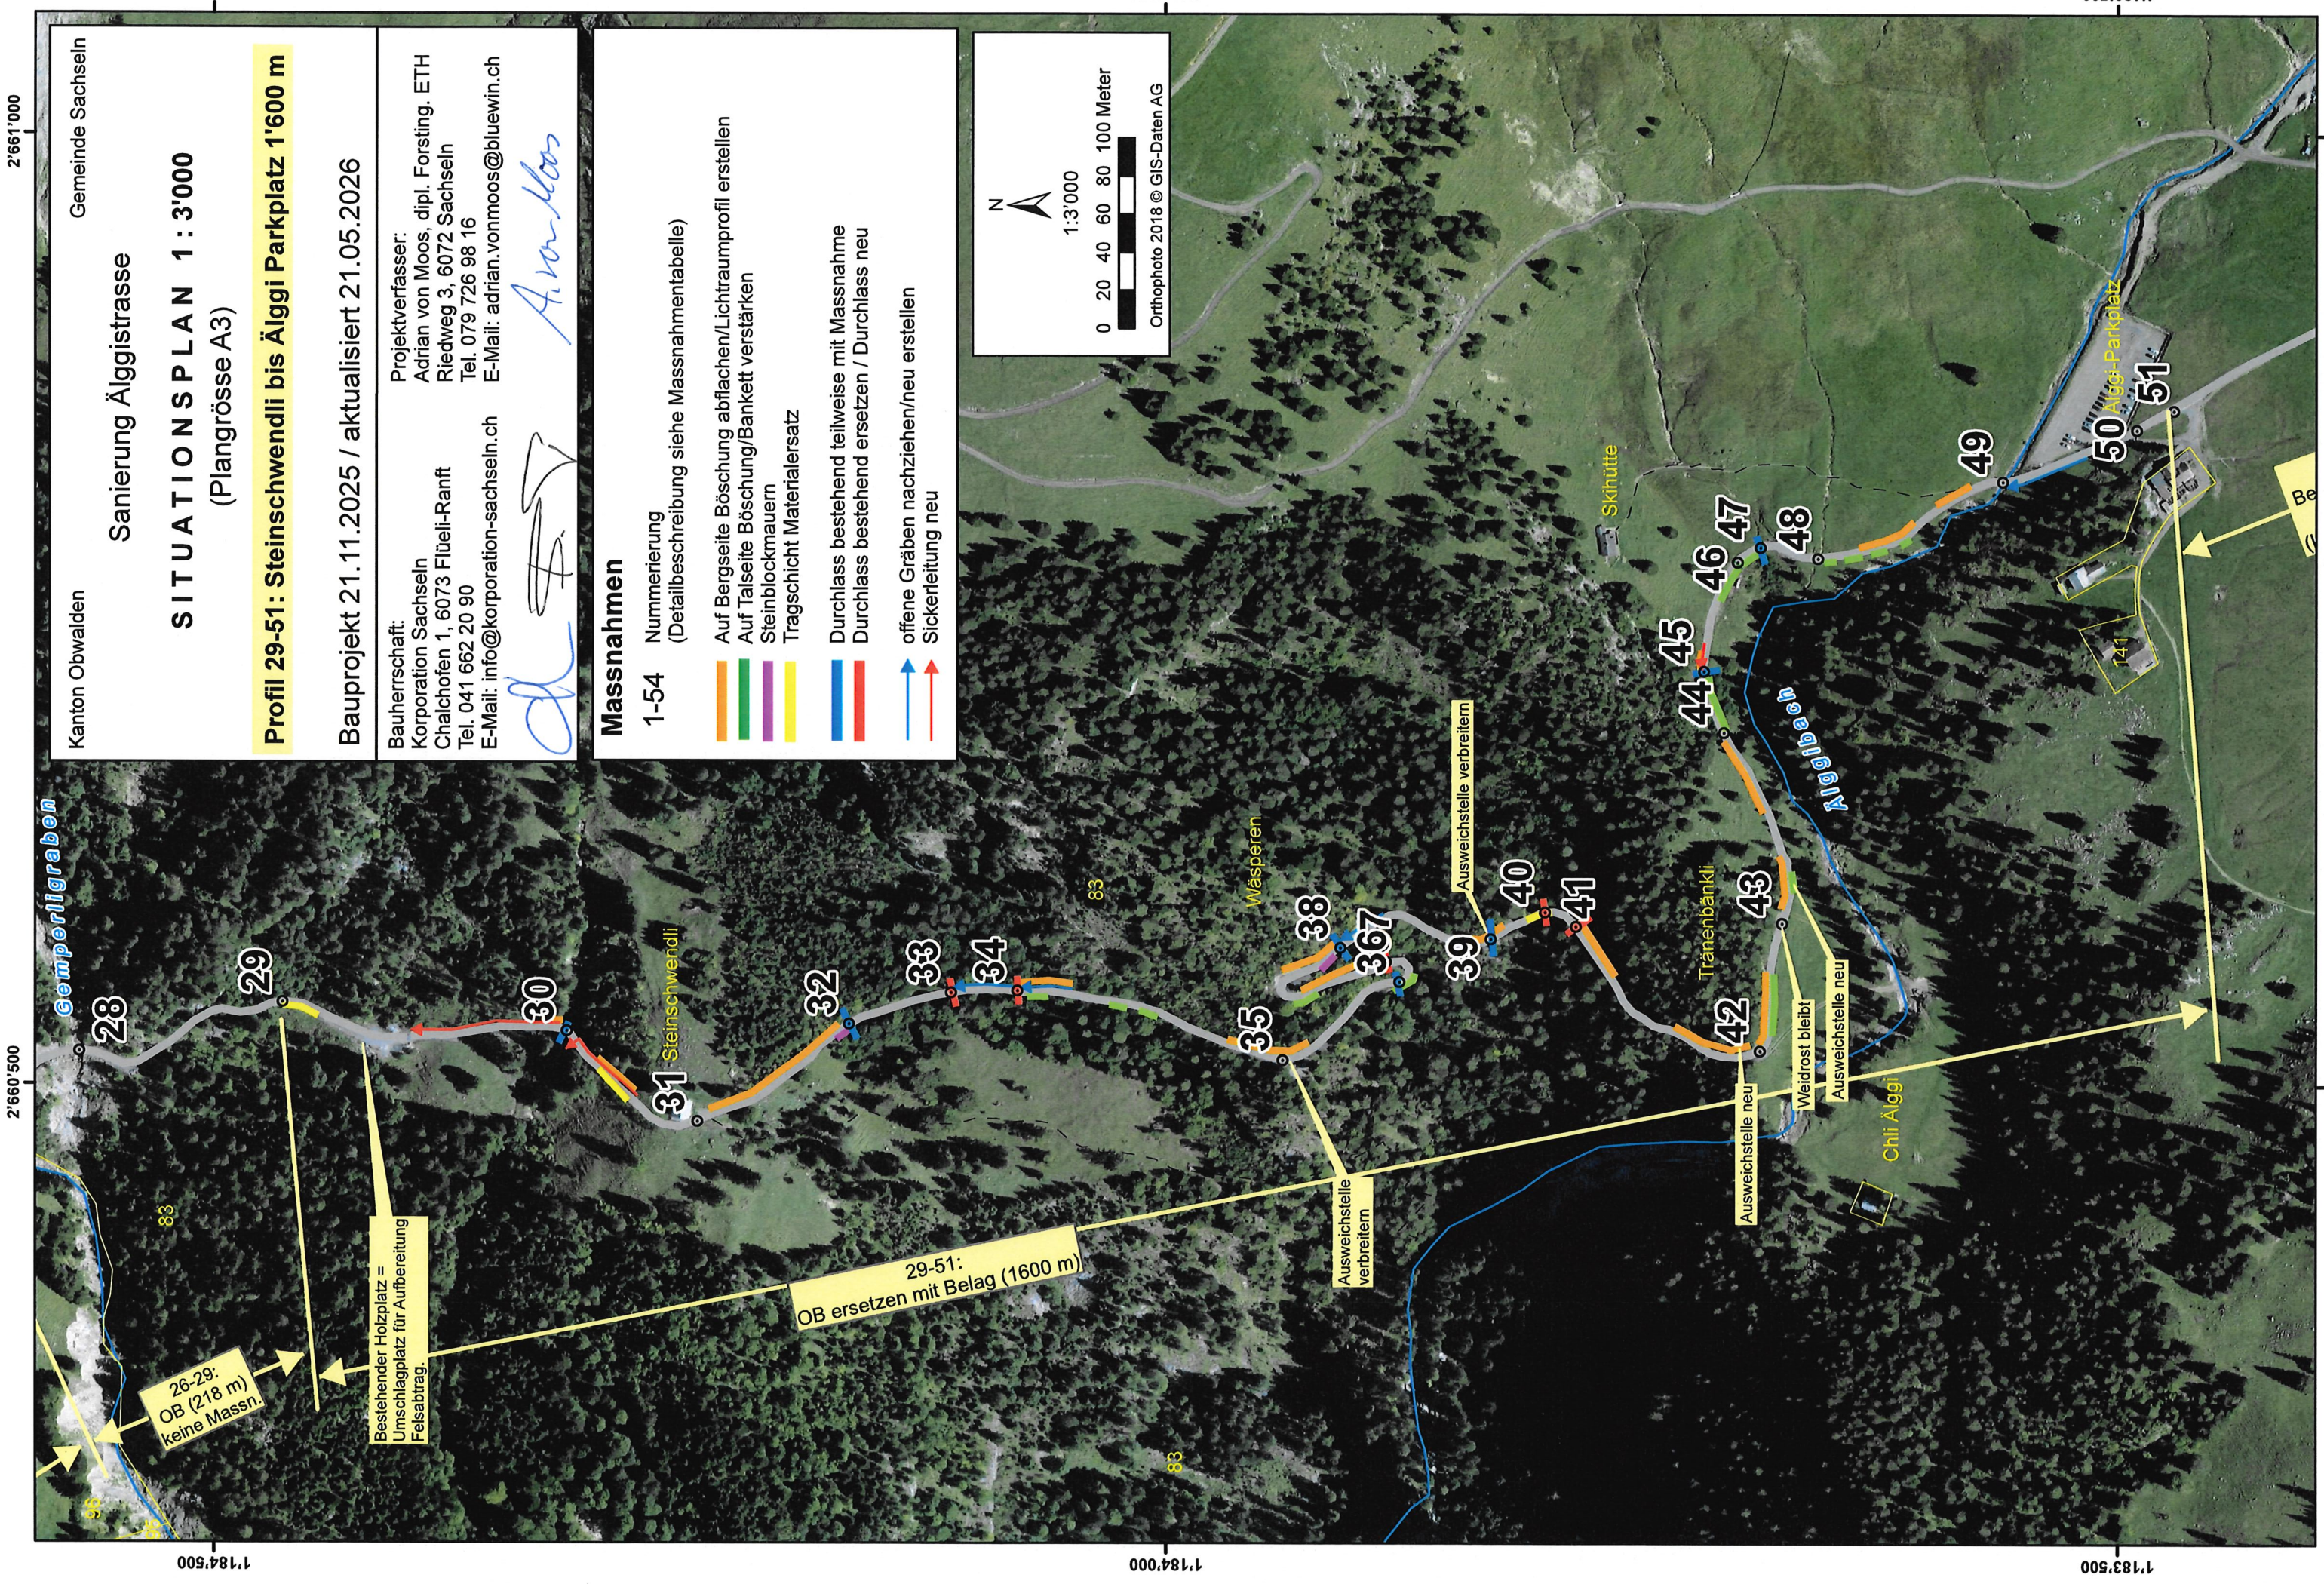

Kanton Obwalden  
Gemeinde Sachseln  
Sanierung Älggstrasse  
**SITUATION PLAN 1 : 3'000**  
(Plangrösse A3)

**Profil 29-51: Steinschwendli bis Äggi Parkplatz 1'600 m**  
Bauprojekt 21.11.2025 / aktualisiert 21.05.2026

Bauherrschaft:  
Korporation Sachseln  
Chalchhofen 1, 6073 Flüeli-Ranft  
Tel. 041 662 20 90  
E-Mail: info@korporation-sachseln.ch

Projektverfasser:  
Adrian von Moos, dipl. Forsting. ETH  
Riedweg 3, 6072 Sachseln  
Tel. 079 726 98 16  
E-Mail: adrian.vonmoos@bluewin.ch

- Massnahmen**
- 1-54 Nummerierung  
(Detailbeschreibung siehe Massnahmenabelle)
- Auf Bergseite Böschung abflachen/Lichttraumprofil erstellen
  - Auf Talseite Böschung/Bankett verstärken
  - Steinblockmauern
  - Tragschicht Materialersatz
  - Durchlass bestehend teilweise mit Massnahme
  - Durchlass bestehend ersetzen / Durchlass neu
  - offene Gräben nachziehen/neu erstellen
  - Sickerleitung neu

N

1:3'000

0 20 40 60 80 100 Meter

Orthophoto 2018 © GIS-Daten AG

26-29:  
OB (218 m)  
keine Massn.

Bestehender Holzplatz =  
Umschlagplatz für Aufbereitung  
Felsabtrag.

29-51:  
OB ersetzen mit Belag (1600 m)

Ausweichstelle  
verbreitern

Ausweichstelle verbreitern

Ausweichstelle neu

Weidrost bleibt

Ausweichstelle neu

Chli Äggi

Tränenbänkli

Skihütte

50 Äggi-Parkplatz

2'660'000

2'659'500

1'186'000

1'185'500

2'659'500

2'660'000

Kanton Obwalden

Gemeinde Sachseln

Sanierung Äggstrasse

**SITUATION S PLAN 1 : 3'000**  
(Plangrösse A3)

**Profil 8-13: Rindelsgr. bis Brandegggr. 1'185 m**

Bauprojekt 21.11.2025 / aktualisiert 21.05.2026

Bauherrschaft:

Korporation Sachseln  
Chalchhofen 1, 6073 Flüeli-Ranft  
Tel. 041 662 20 90  
E-Mail: [info@korporation-sachseln.ch](mailto:info@korporation-sachseln.ch)

Projektverfasser:  
Adrian von Moos, dipl. Forsting. ETH  
Riedweg 3, 6072 Sachseln  
Tel. 079 726 98 16  
E-Mail: [adrian.vonmoos@bluewin.ch](mailto:adrian.vonmoos@bluewin.ch)

*Adrian von Moos*

## Massnahmen

- 1-54** Nummerierung  
(Detailbeschreibung siehe Massnahmentabelle)
- Auf Bergseite Böschung abflachen/Lichttraumprofil erstellen
  - Auf Talseite Böschung/Bankett verstärken
  - Steinblockmauern
  - Tragschicht Materialersatz
  - Durchlass bestehend teilweise mit Massnahme
  - Durchlass bestehend ersetzen / Durchlass neu
  - offene Gräben nachziehen/neu erstellen
  - Sickerleitung neu



1:3'000

0 20 40 60 80 100 Meter

Orthophoto 2018 © GIS-Daten AG

10-11:  
Betonfahrbahn, defekte Stellen reparieren  
(592 m)

6-10:  
OB ersetzen mit  
Belag (382 m)

11-13:  
OB ersetzen mit  
Belag (391 m)

13-14: Beton (60 m)

Ausweichstelle neu

Ausweichstelle verlängern

Fundament  
sichern

Weidrost aufheben  
Ausweichstelle verlängern

Weidrost aufheben

Weidrost aufheben

Rindelsgraben

Brandegggraben

Rindel



2'659'000 1'187'000 2'659'500 1'186'500

Kanton Obwalden Gemeinde Sachseln

Sanierung Älggstrasse

## SITUATION PLAN 1 : 3'000 (Plangrösse A3)

**Profil 1-8: Blatten bis Rindelsgraben 1'155 m**

Bauprojekt 21.11.2025 / aktualisiert 21.05.2026

Bauherrschaft:

Korporation Sachseln  
Chalchofen 1, 6073 Flüeli-Ranft  
Tel. 041 662 20 90  
E-Mail: info@korporation-sachseln.ch

Projektverfasser:  
Adrian von Moos, dipl. Forsting. ETH  
Riedweg 3, 6072 Sachseln  
Tel. 079 726 98 16  
E-Mail: adrian.vonmoos@bluewin.ch

*Adrian von Moos*

*[Signature]*

### Massnahmen


- 1-54 Nummerierung  
(Detailbeschreibung siehe Massnahmenabelle)
- Auf Bergseite Böschung abflachen/Lichttraumprofil erstellen
  - Auf Talseite Böschung/Bankett verstärken
  - Steinblockmauern
  - Tragschicht Materialersatz
  - Durchlass bestehend teilweise mit Massnahme
  - Durchlass bestehend ersetzen / Durchlass neu
  - offene Gräben nachziehen/neu erstellen
  - Sickerleitung neu



1:3'000

0 20 40 60 80 100 Meter

Orthophoto 2018 © GIS-Daten AG

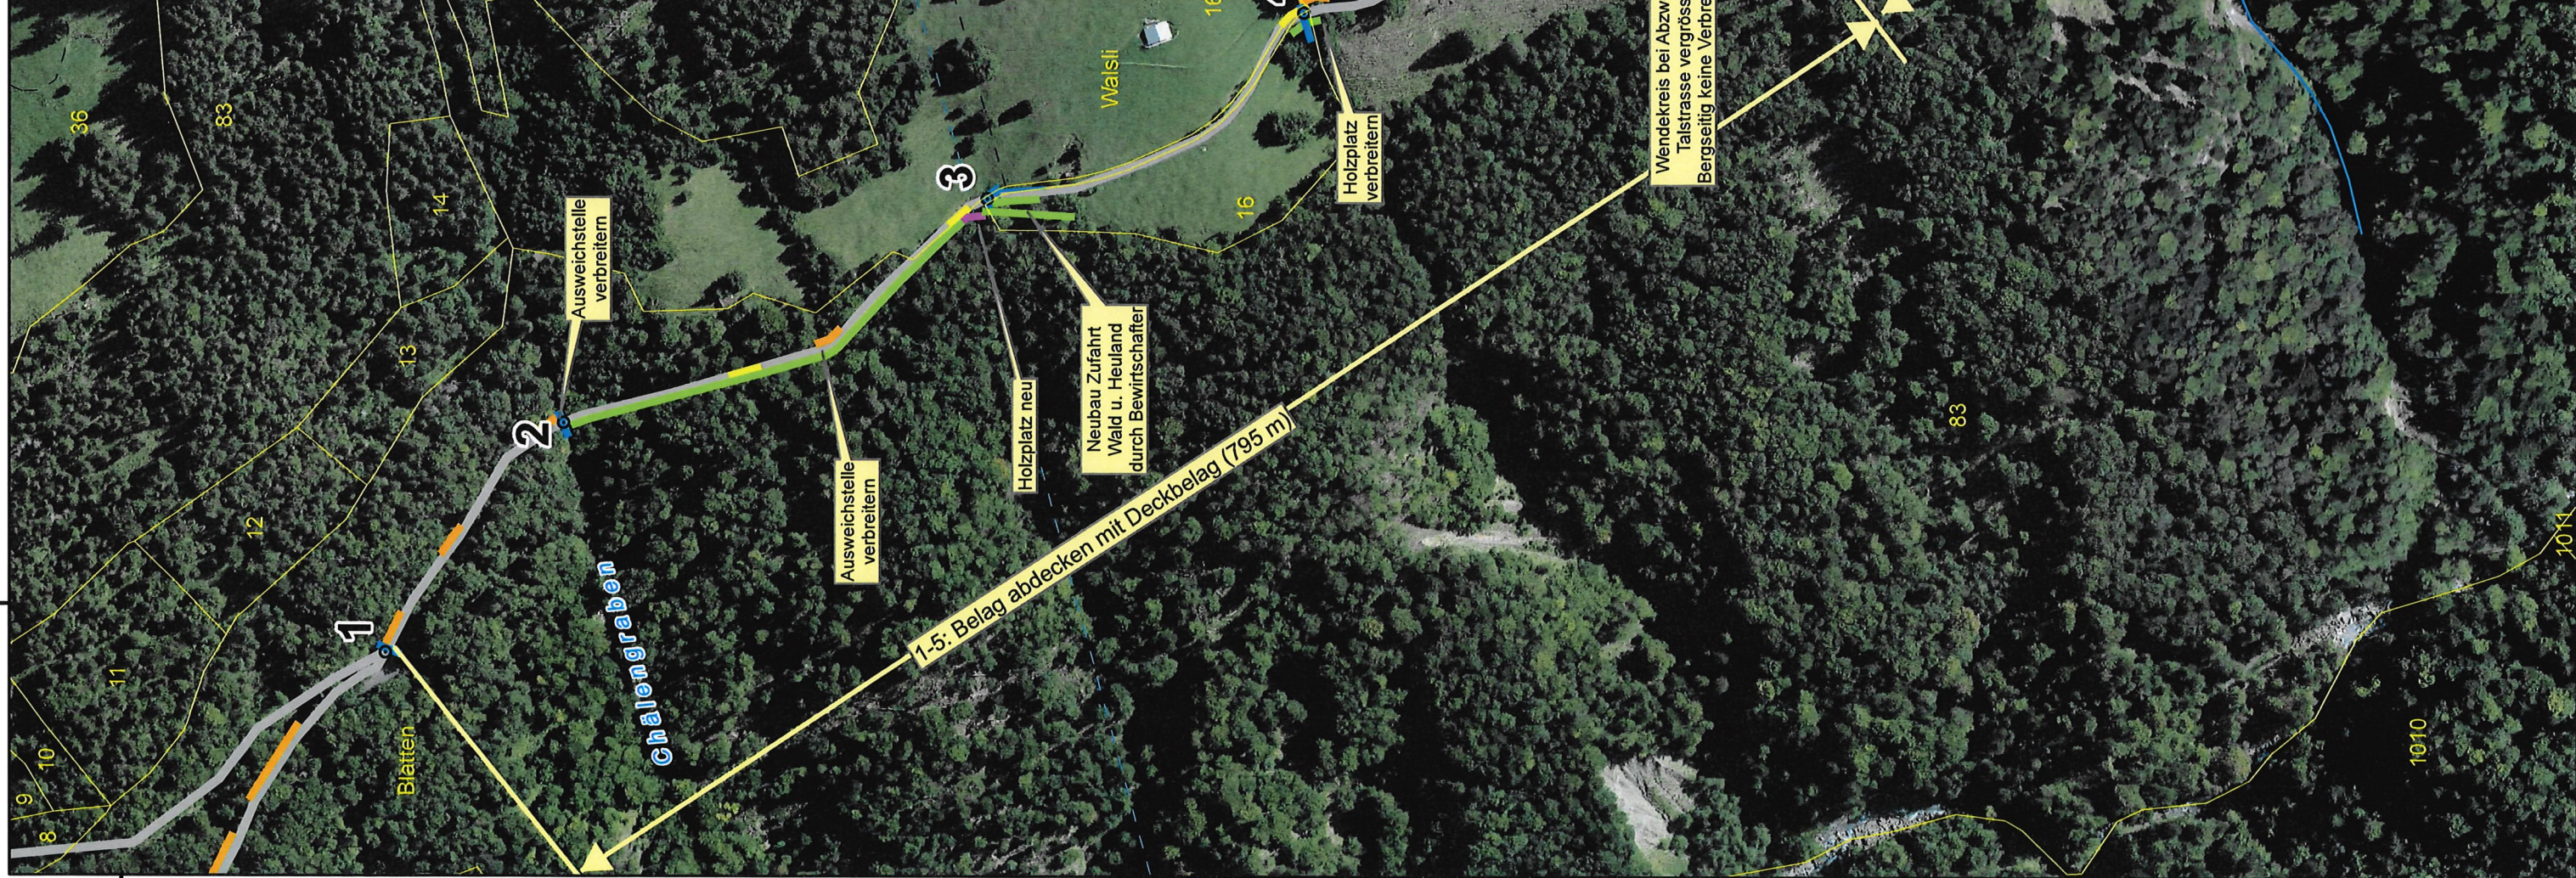

2'659'000

2'659'500